


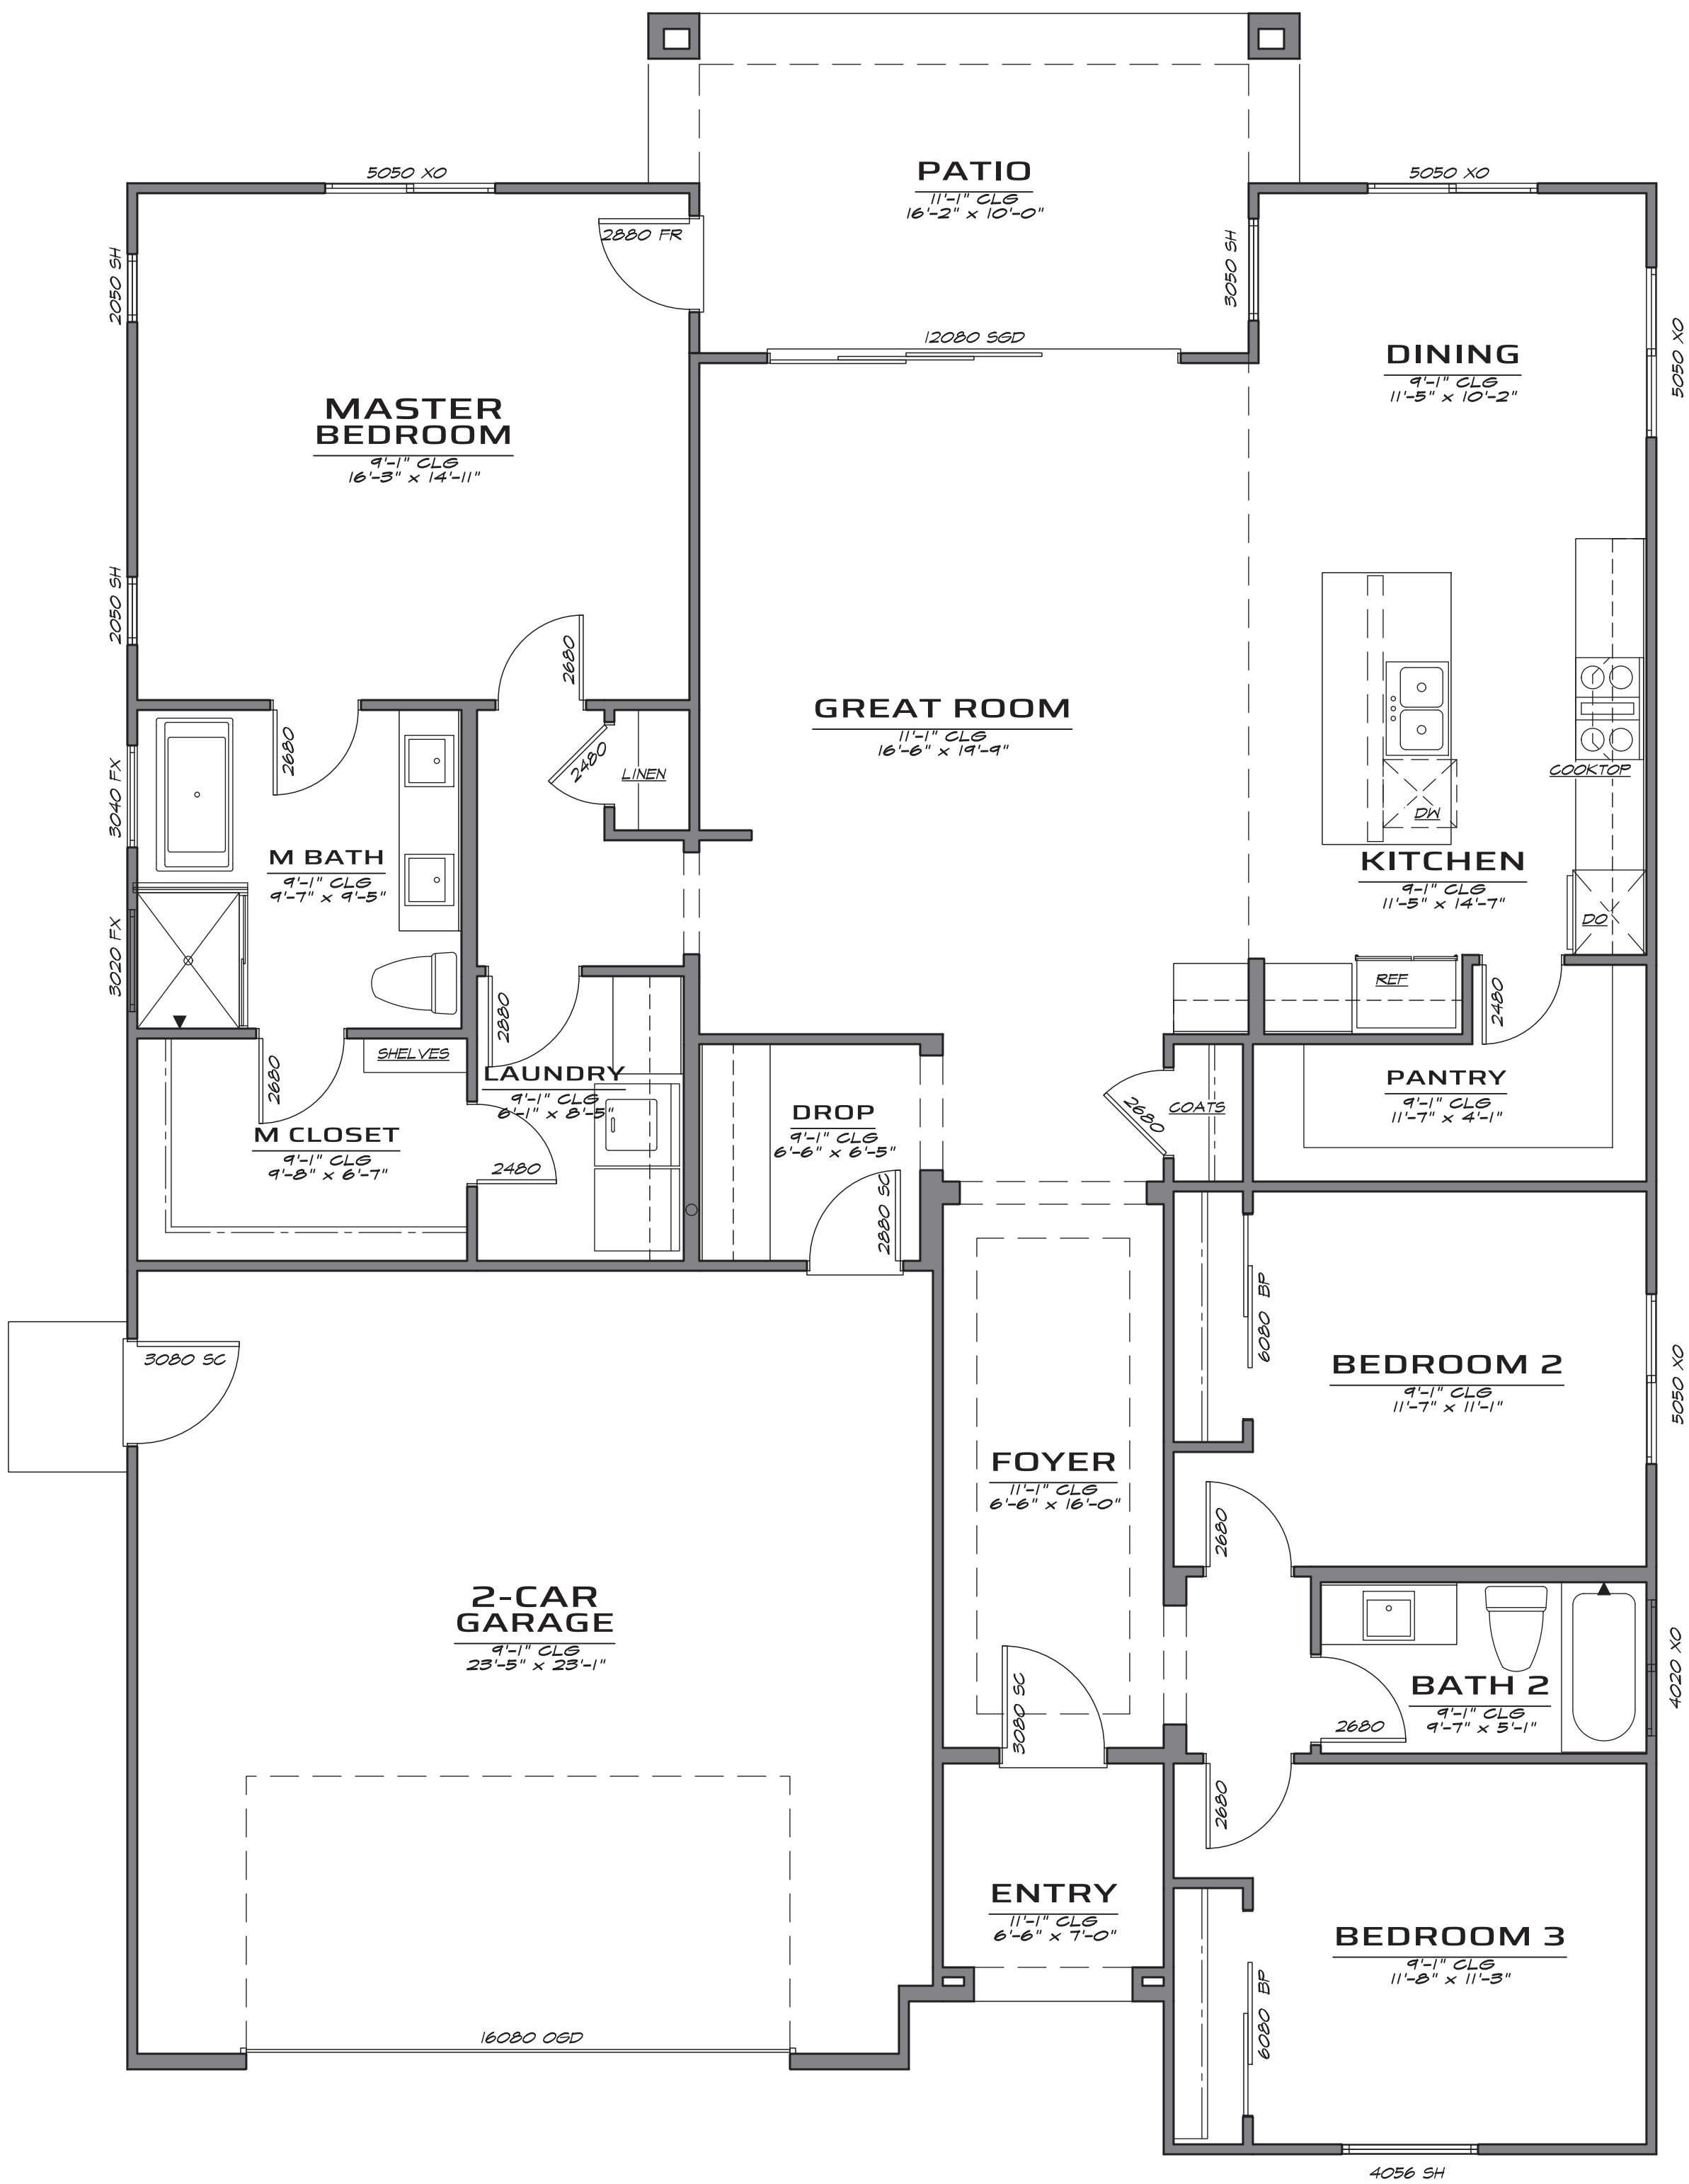

AREA SCHEDULE	
LIVABLE	1835 SQ. FT.
2-CAR GARAGE	538 SQ. FT.
ENTRY	46 SQ. FT.
PATIO	177 SQ. FT.
RESIDENCE TOTAL	2615 SQ. FT.
LOT AREA	44721 SQ. FT.
FOOTPRINT	2615 SQ. FT.
COVERAGE	5.85 %
MAX COVERAGE	??

FLOOR PLAN
SCALE:1/4" = 1'-0"



RIGHT ELEVATION
SCALE: 1/4"=1'-0"



REAR ELEVATION
SCALE: 1/4"=1'-0"



LEFT ELEVATION
SCALE: 1/4"=1'-0"




FRONT ELEVATION
SCALE: 1/4"=1'-0"






FRONT

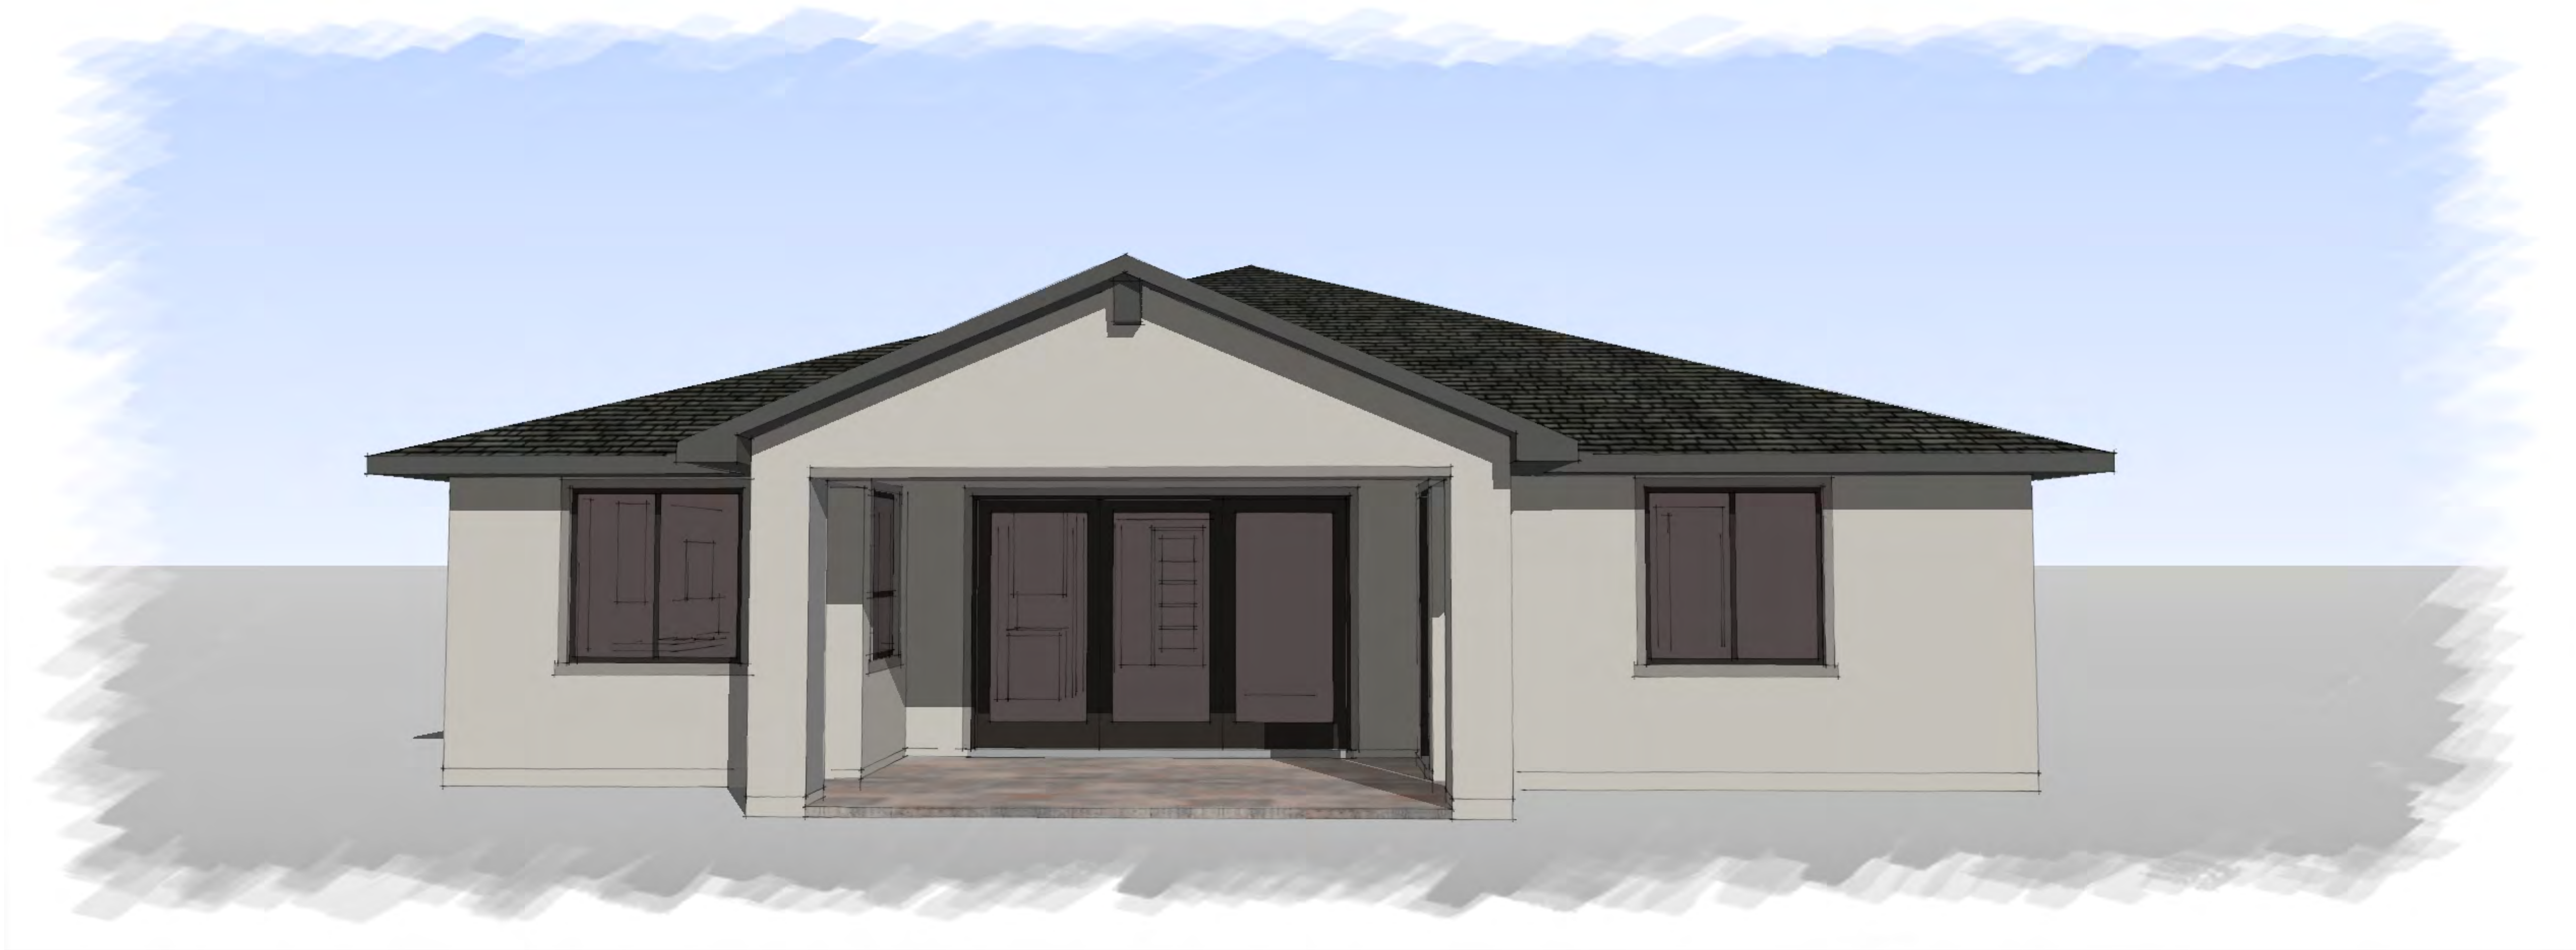

REAR

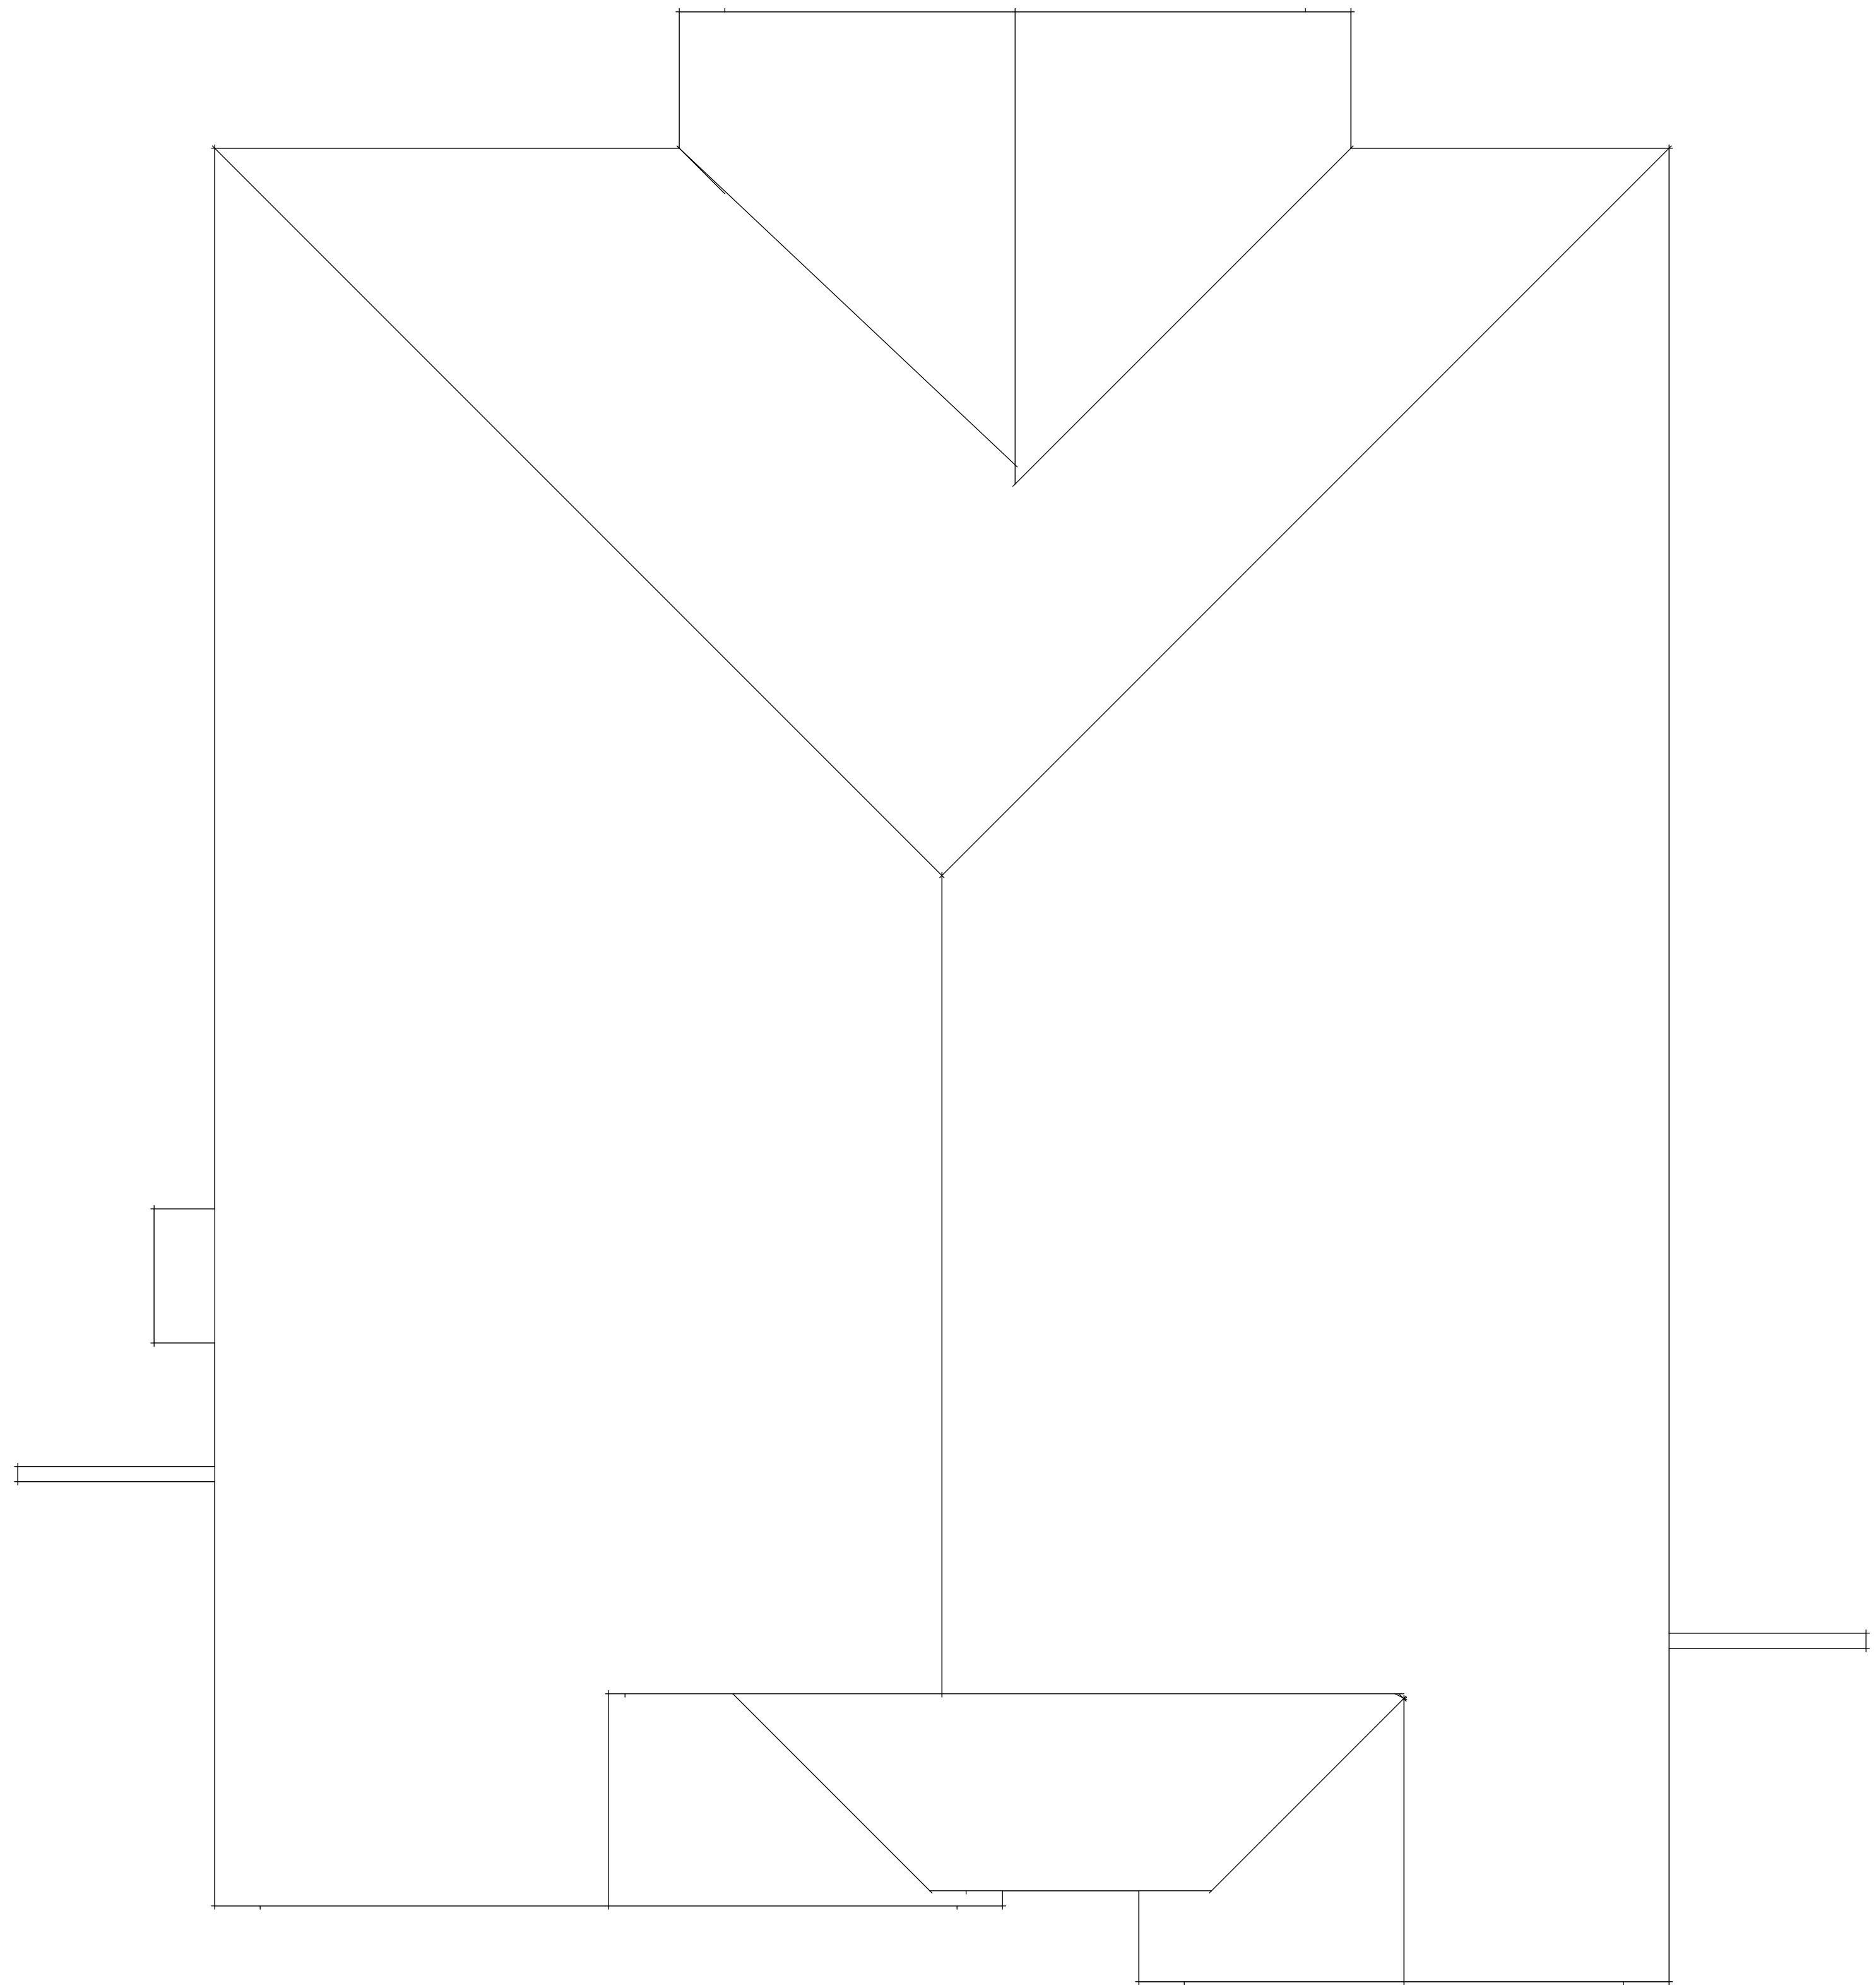

ROOF PLAN
SCALE: 1/4" = 1'-0"