



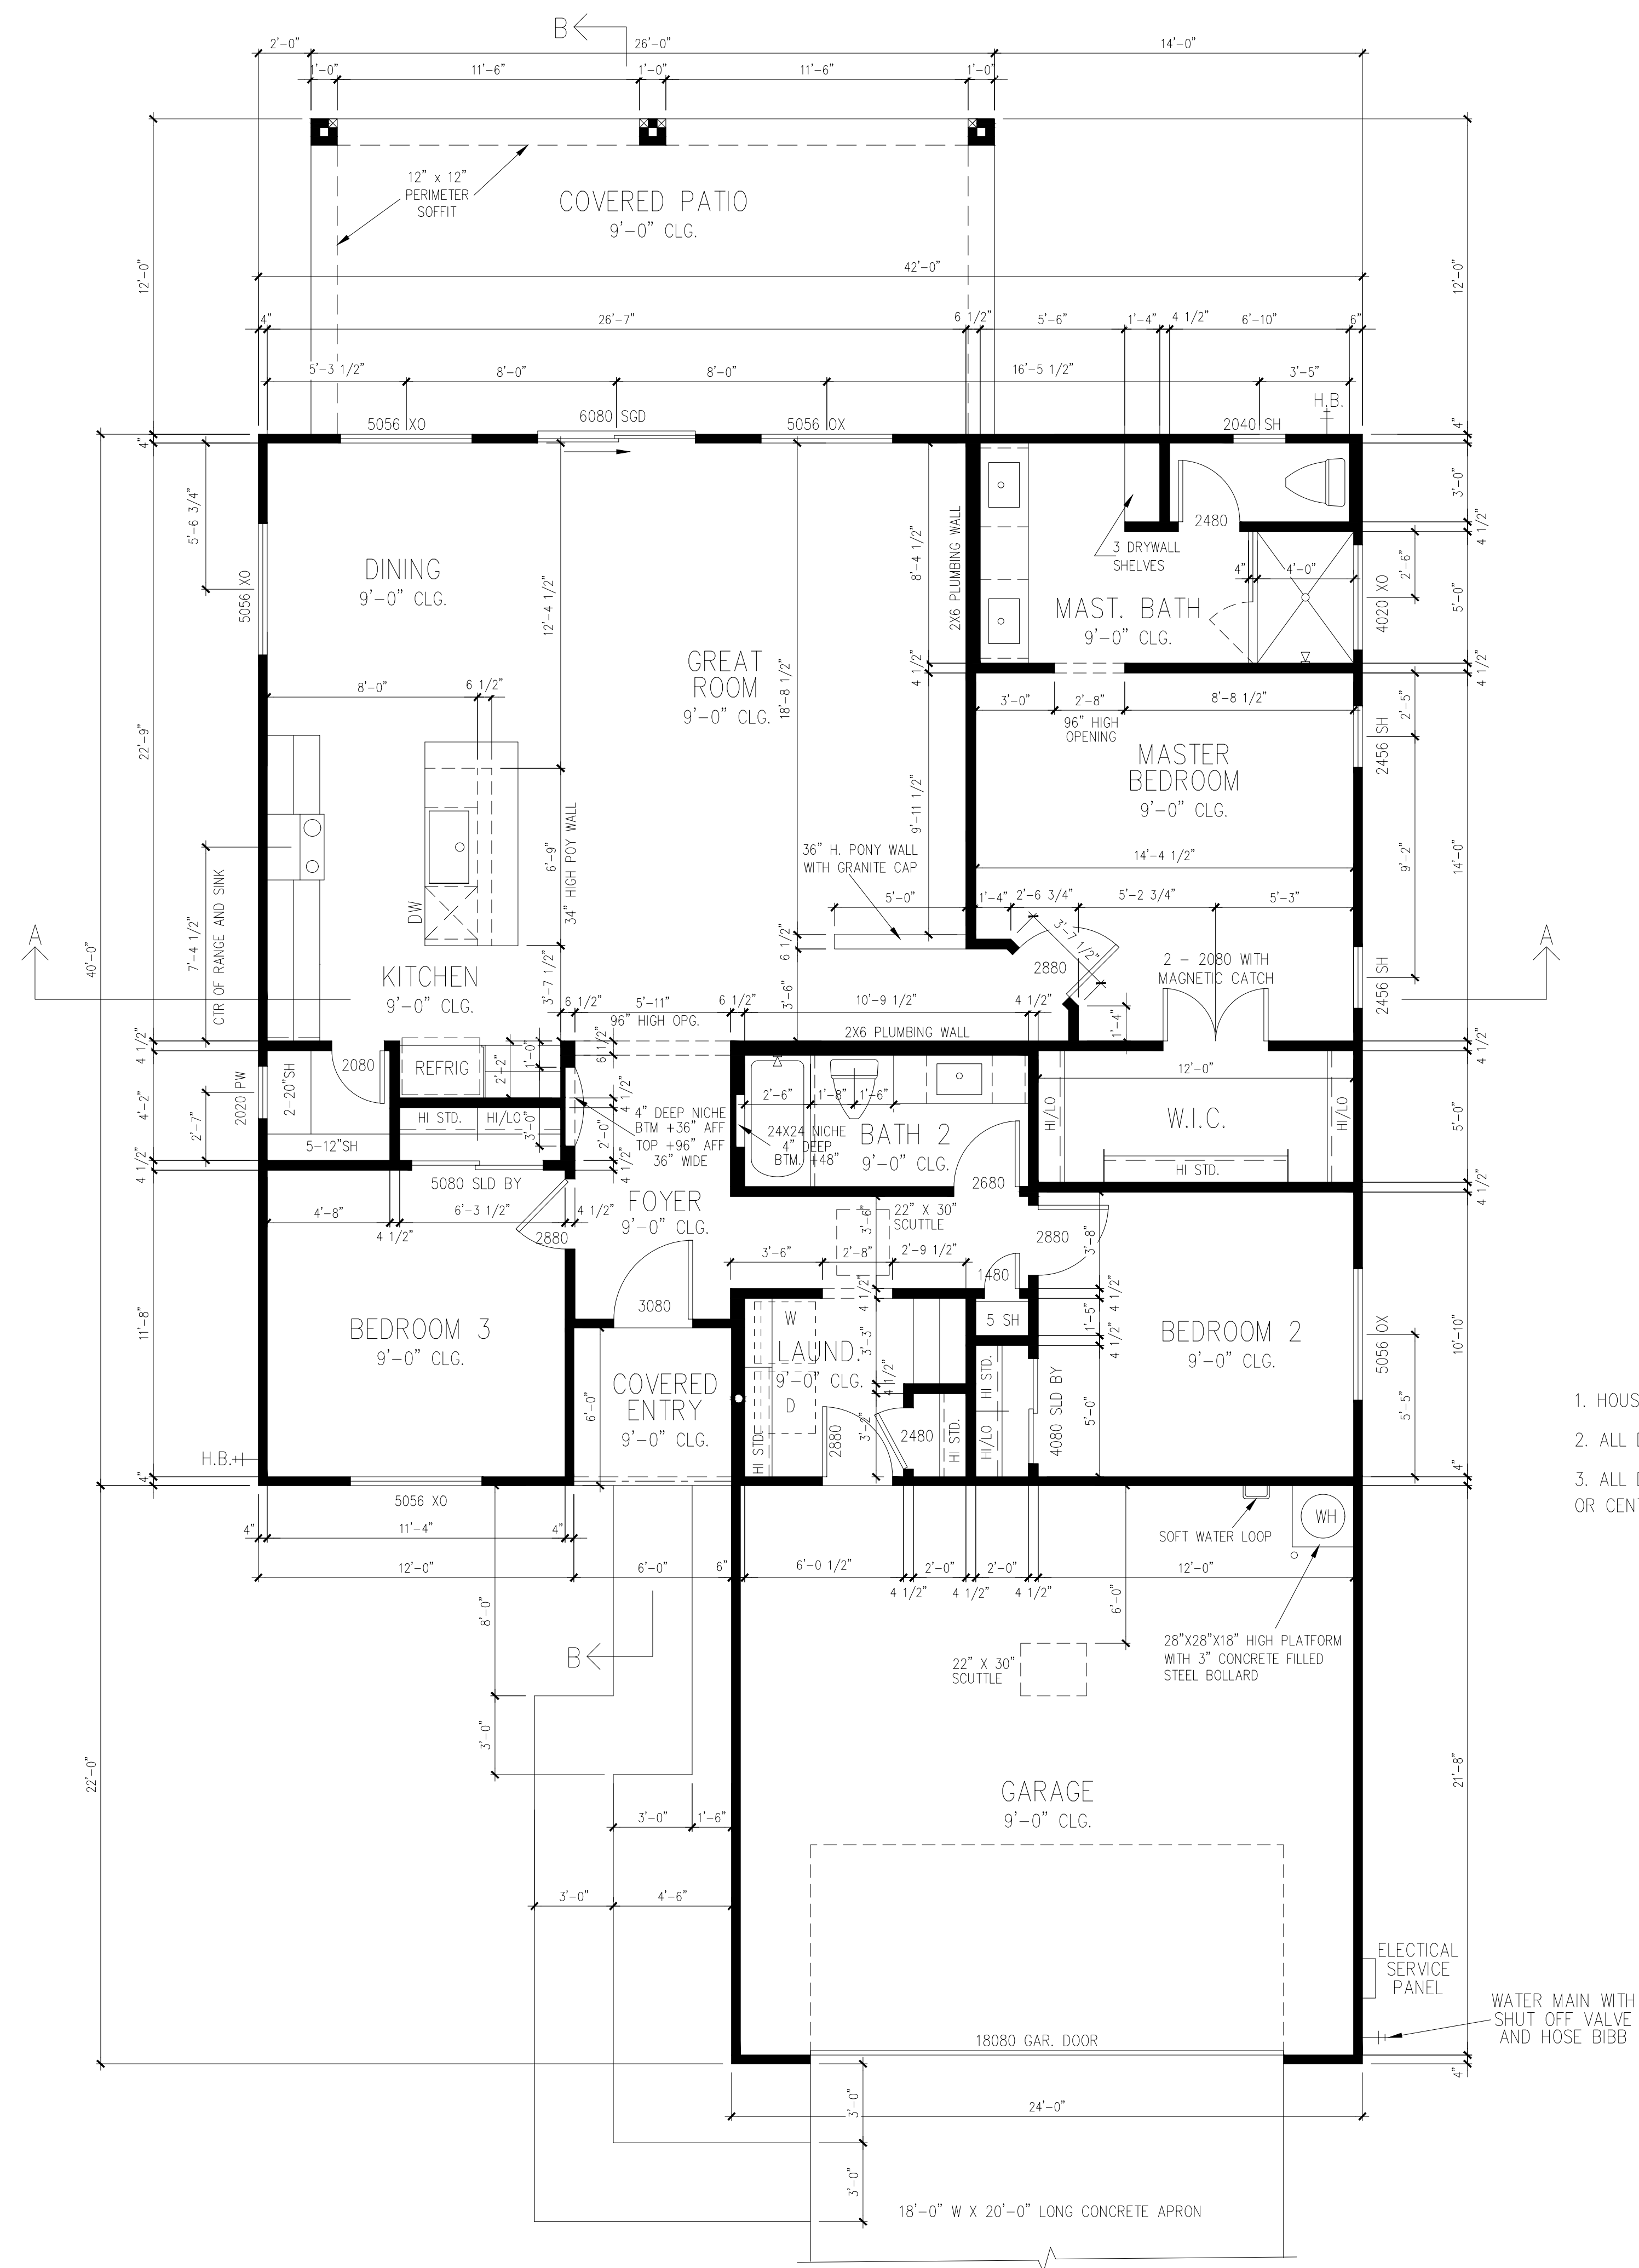


1. HOUSE IS 100% FULLY SHEARED
2. ALL DIMENSIONS ARE TO FINISH DRYWALL
3. ALL DOORS ARE 3 STUDS FROM CORNERS
OR CENTERED UNLESS NOTED OTHERWISE.

FLOOR PLAN

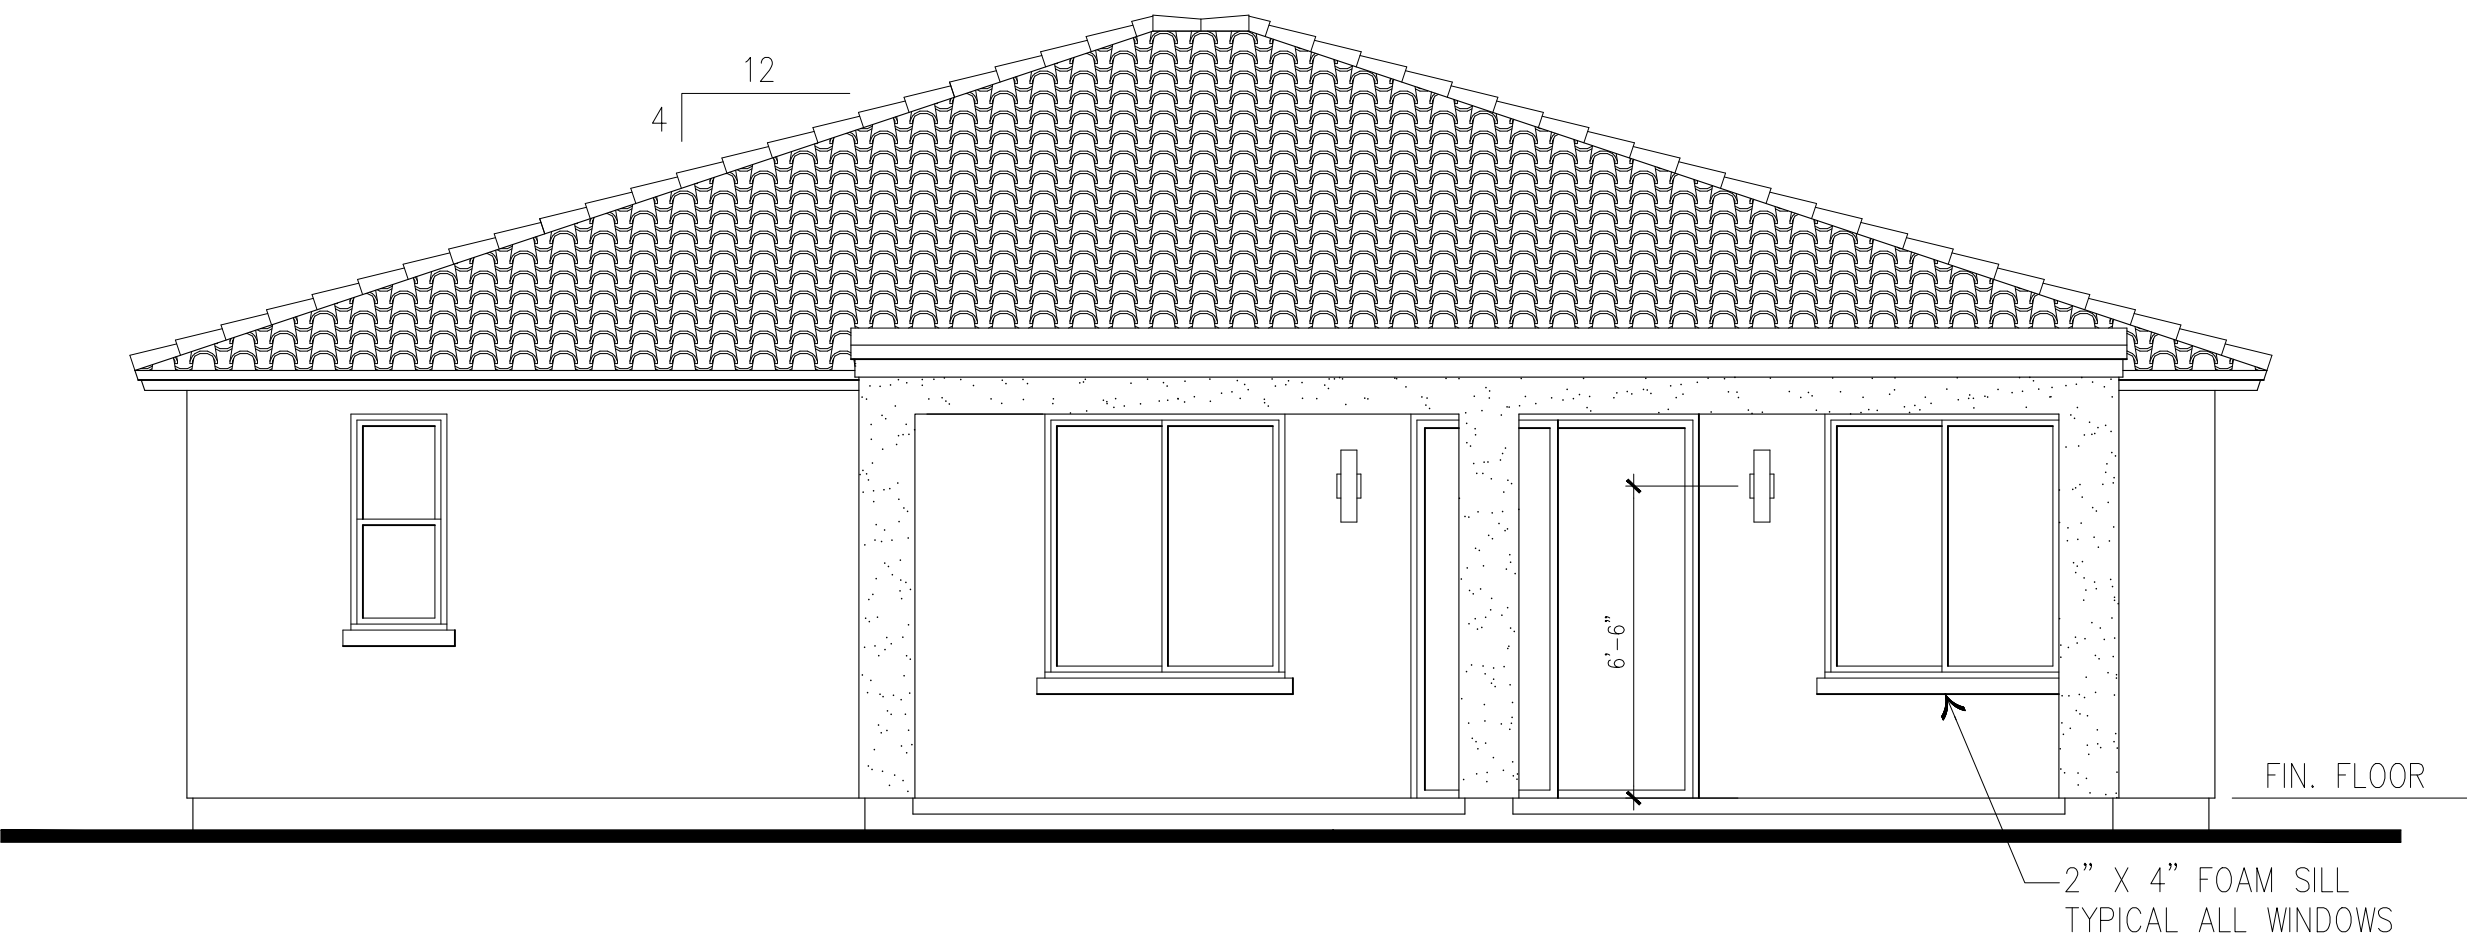


REAR ELEVATION "C"

SCALE: 1/4" = 1'-0"

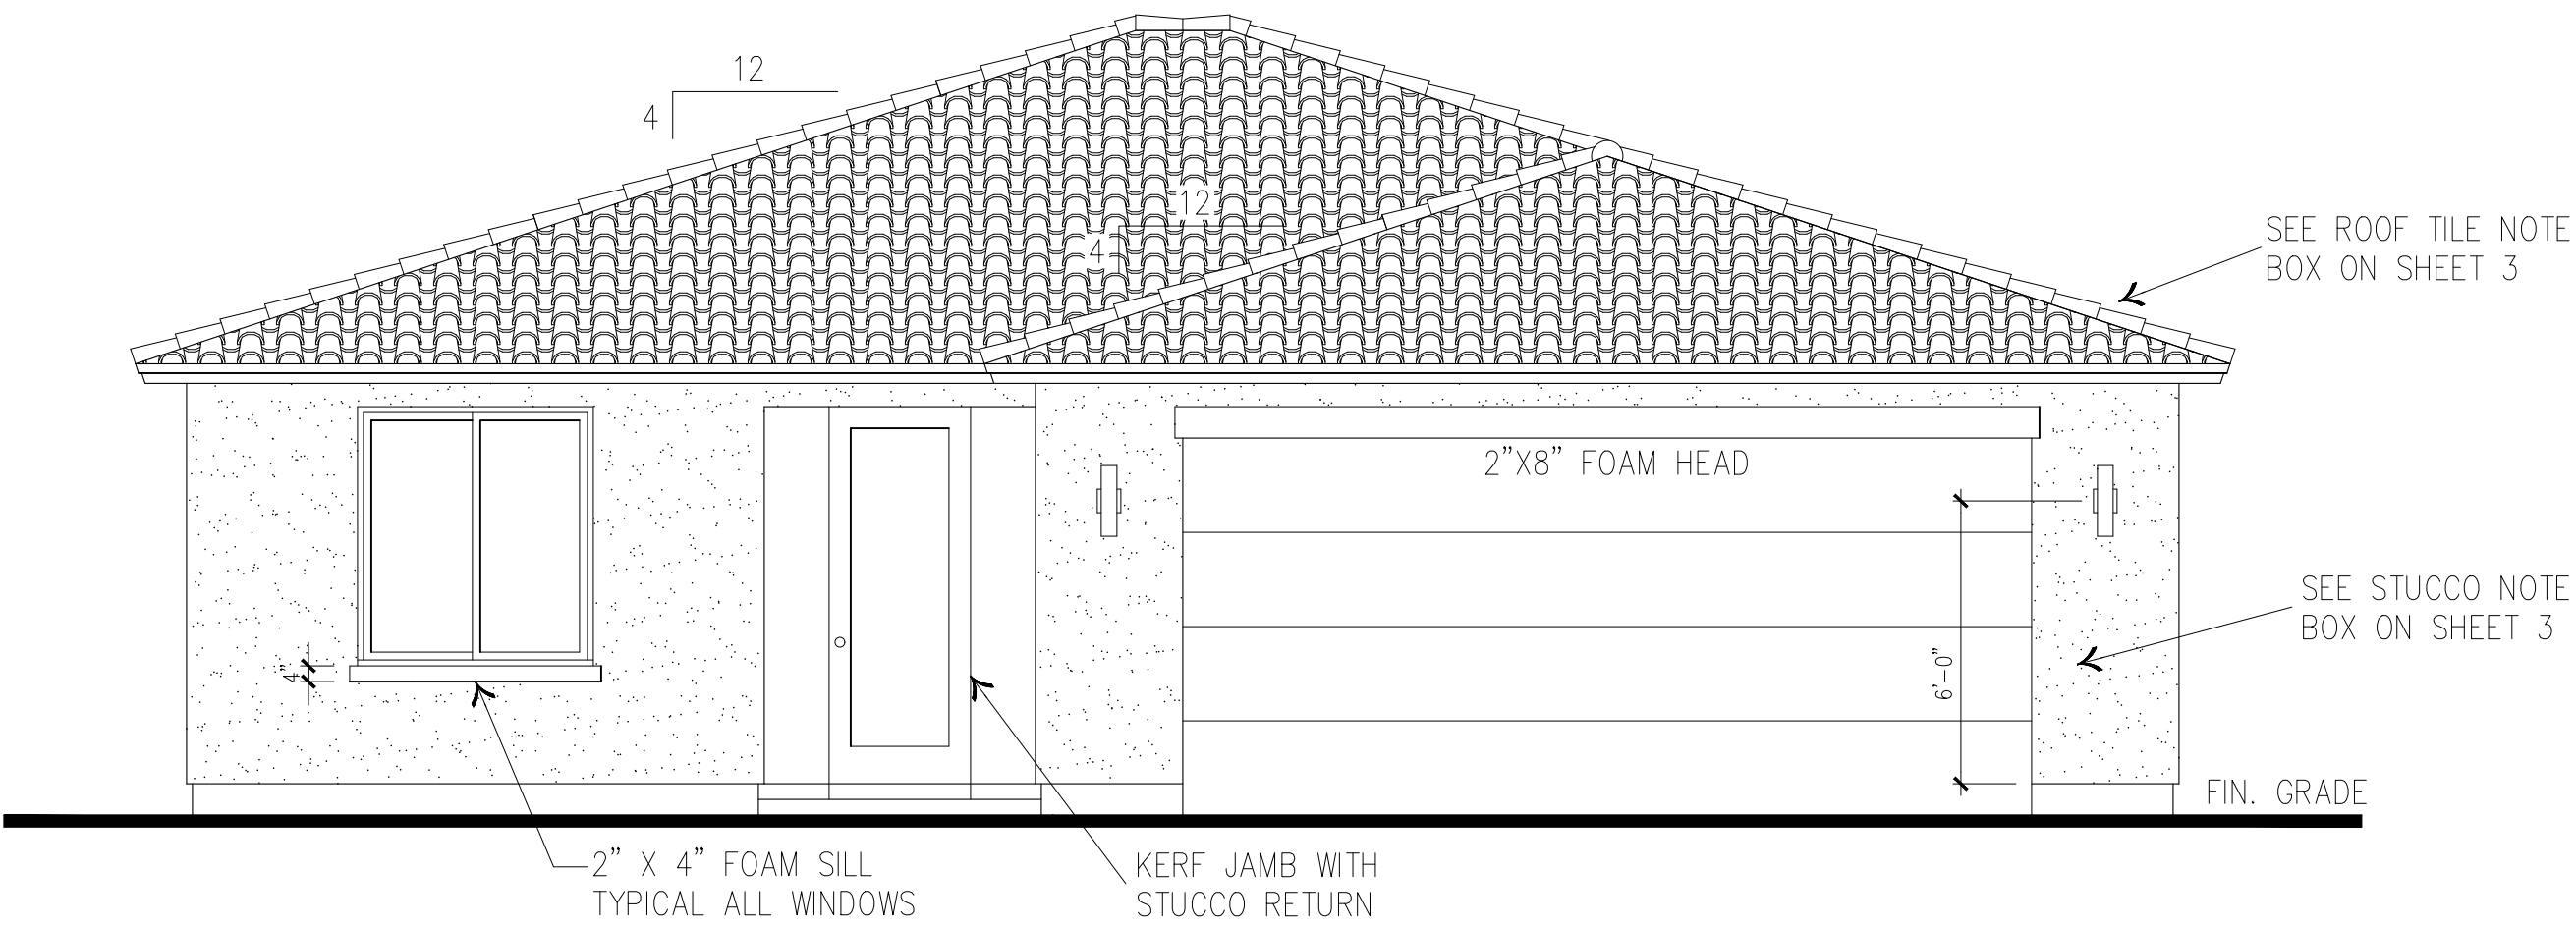


FRONT ELEVATION "C"

SCALE: 1/4" = 1'-0"

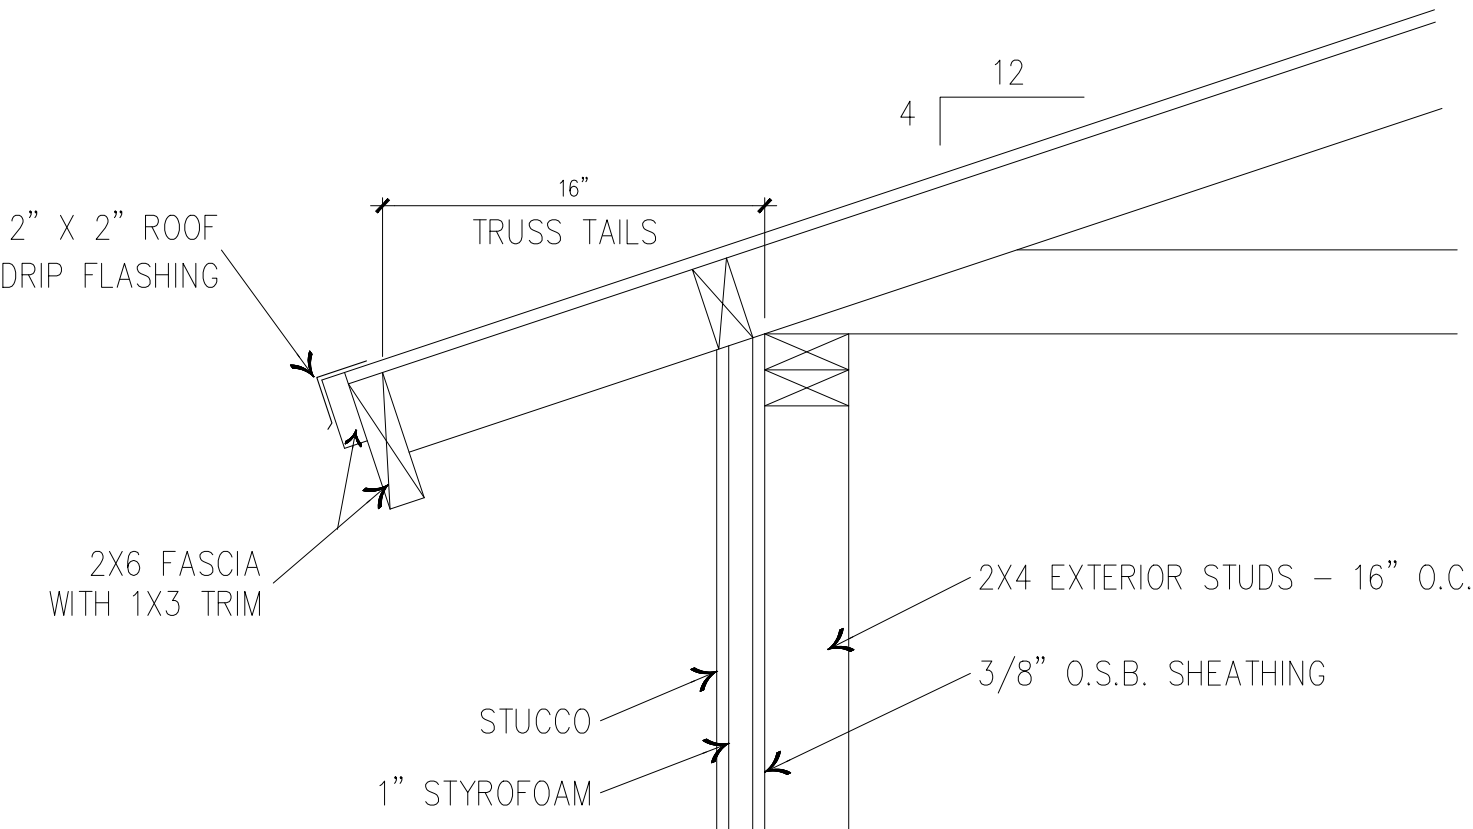


SOFFIT/FASCIA DETAIL

NOT TO SCALE

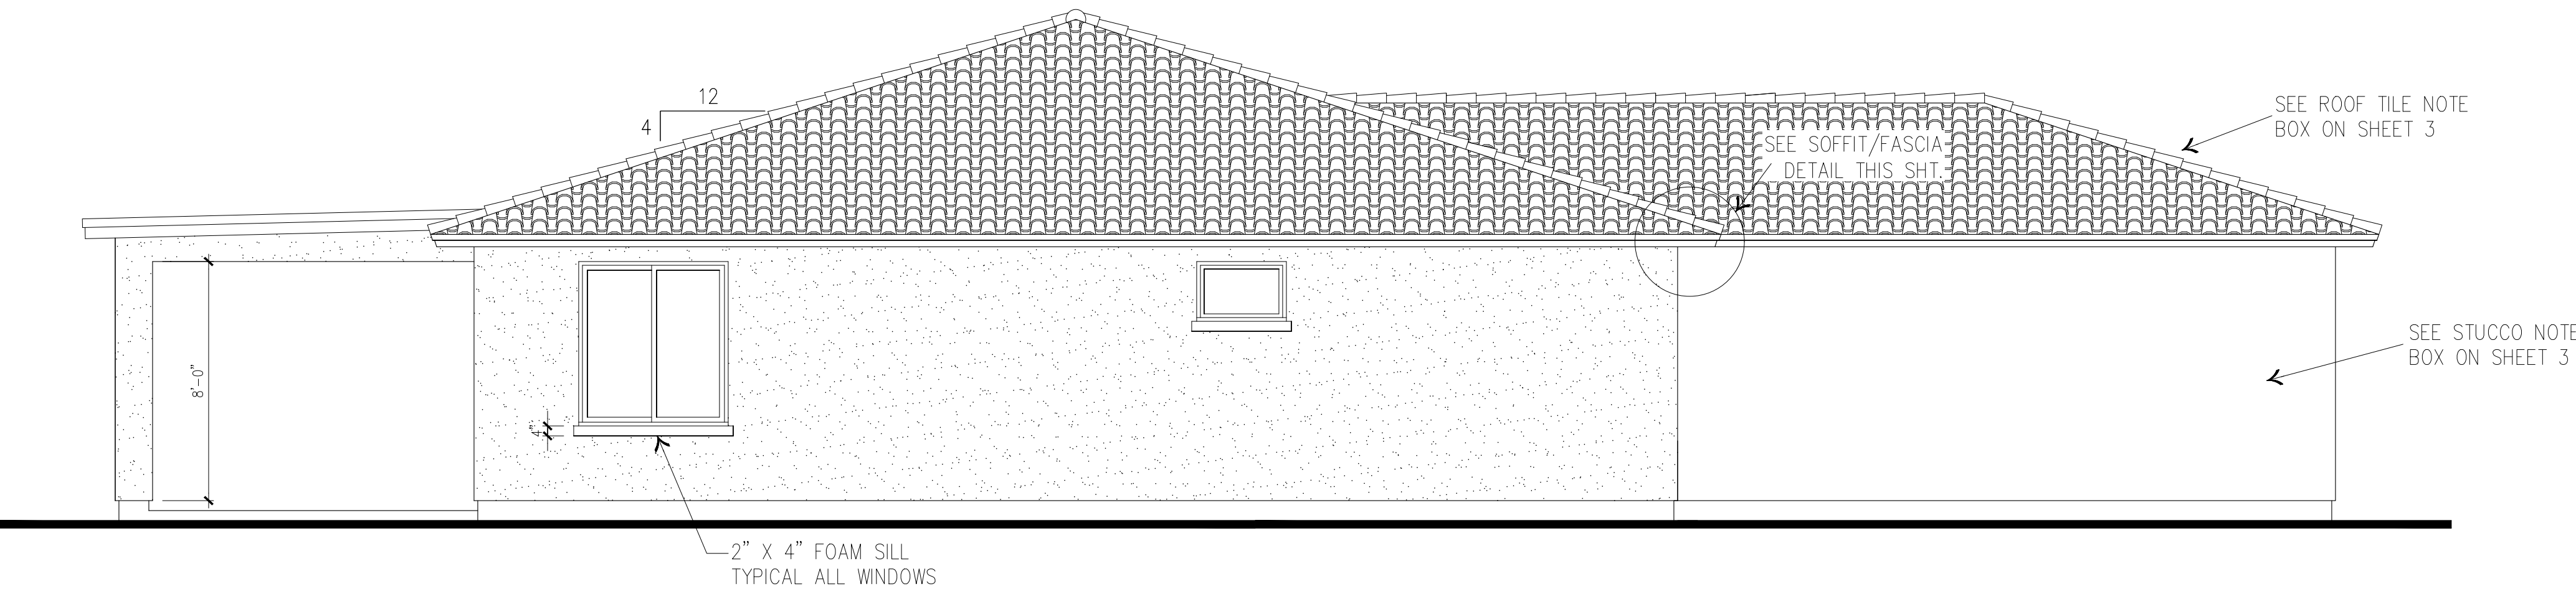

LEFT ELEVATION "C"

SCALE: 1/4" = 1'-0"

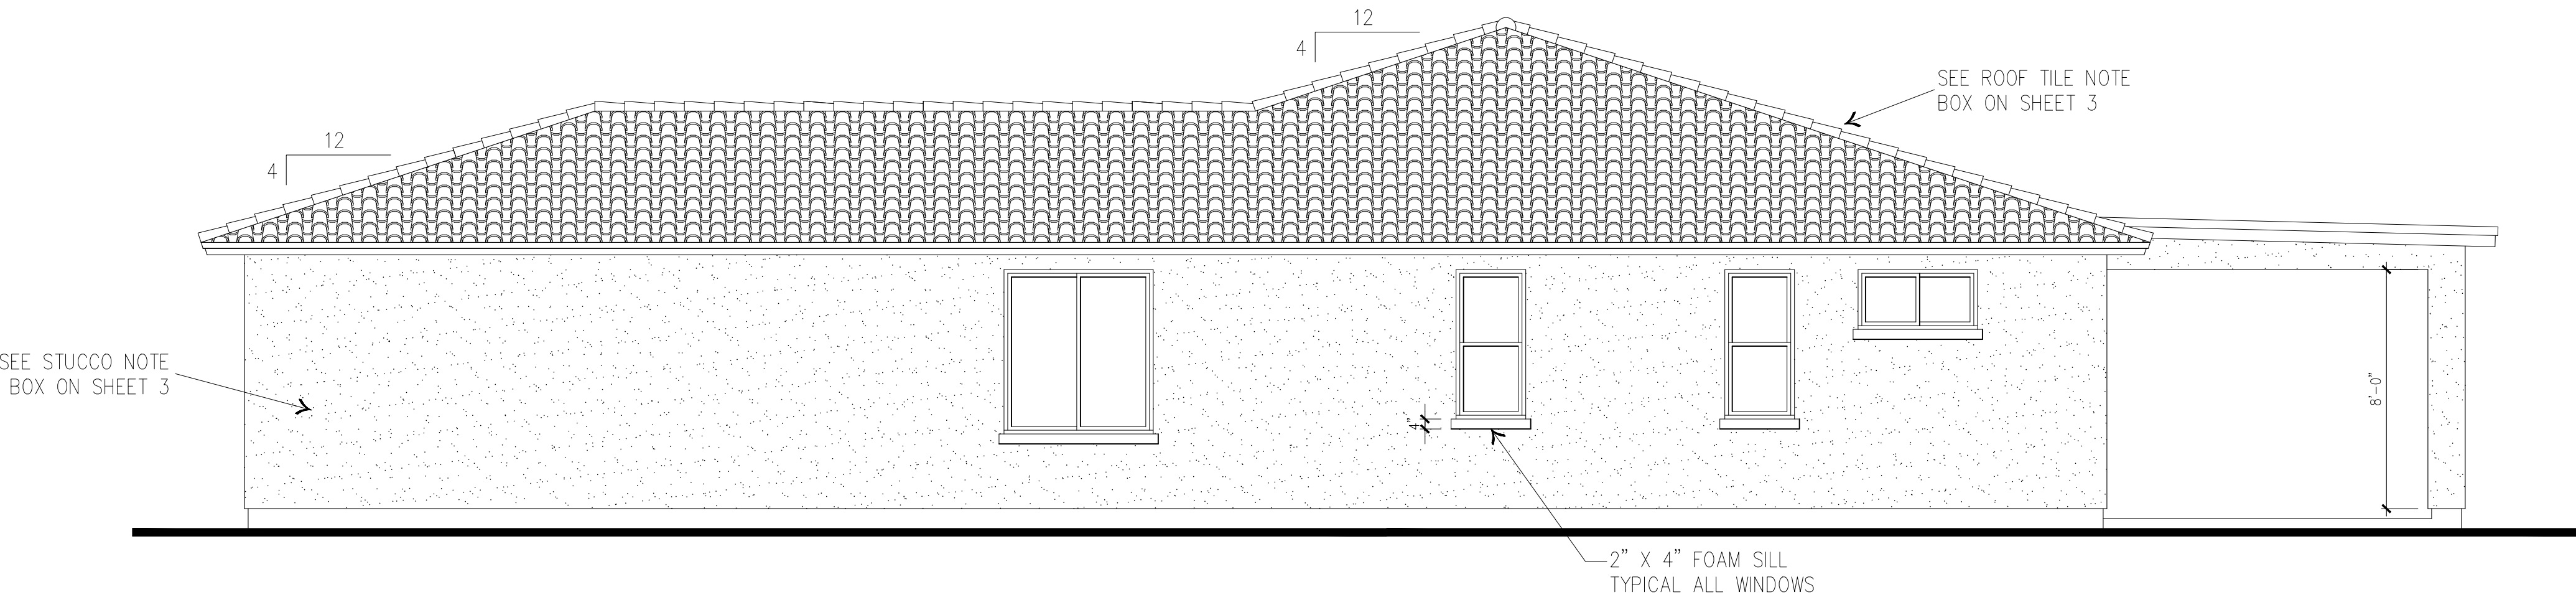

RIGHT ELEVATION "C"

SCALE: 1/4" = 1'-0"

REVISIONS:

1	None
2	None
3	None

1644
PLAN

Phoenix, AZ
602-618-7755



ELEVATION
"C"

JOB NUMBER: 1644 PLAN

CURRENT PLOT DATE: 05/01/2022

ALL
ELEVATIONS

SHT. 3C