



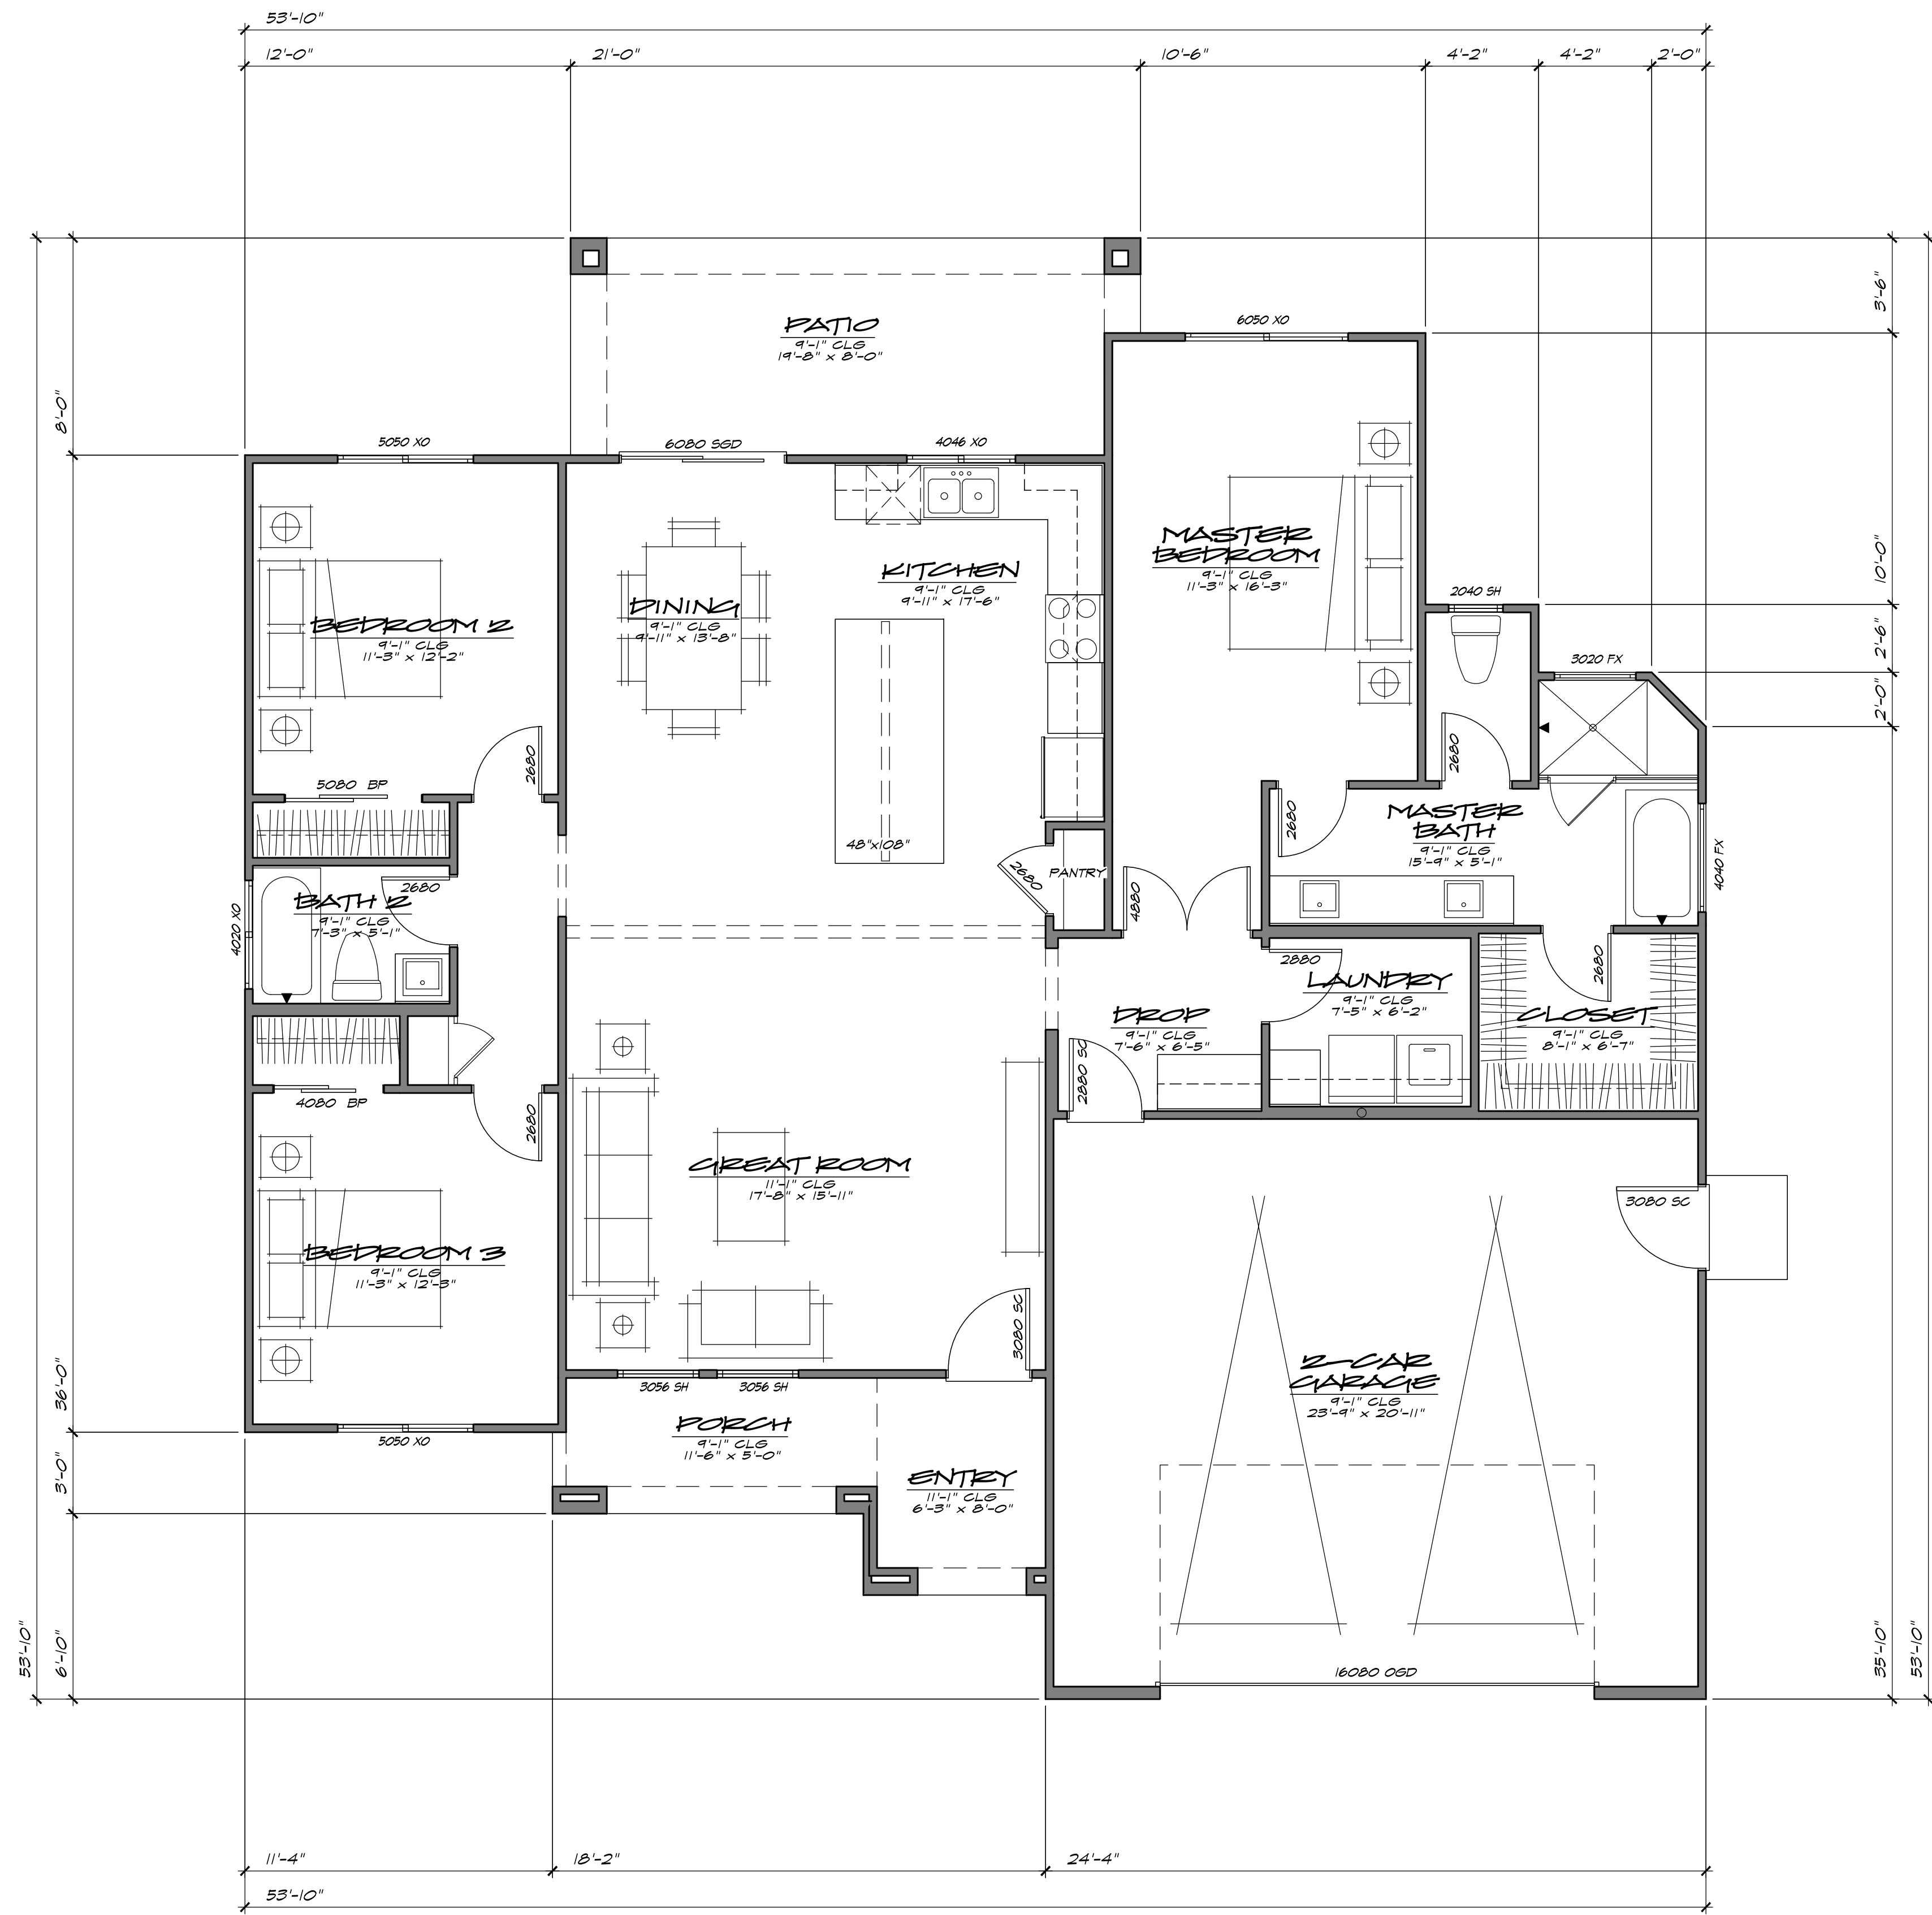

FLOOR PLAN
SCALE: 1/4" = 1'-0"



AREA SCHEDULE	
LIVABLE	1604 SQ. FT.
2-CAR GARAGE	517 SQ. FT.
PORCH	110 SQ. FT.
PATIO	162 SQ. FT.
RESIDENCE TOTAL	2393 SQ. FT.
LOT AREA	*****
FOOTPRINT	2393 SQ. FT.
COVERAGE	*****
MAX COVERAGE	40%

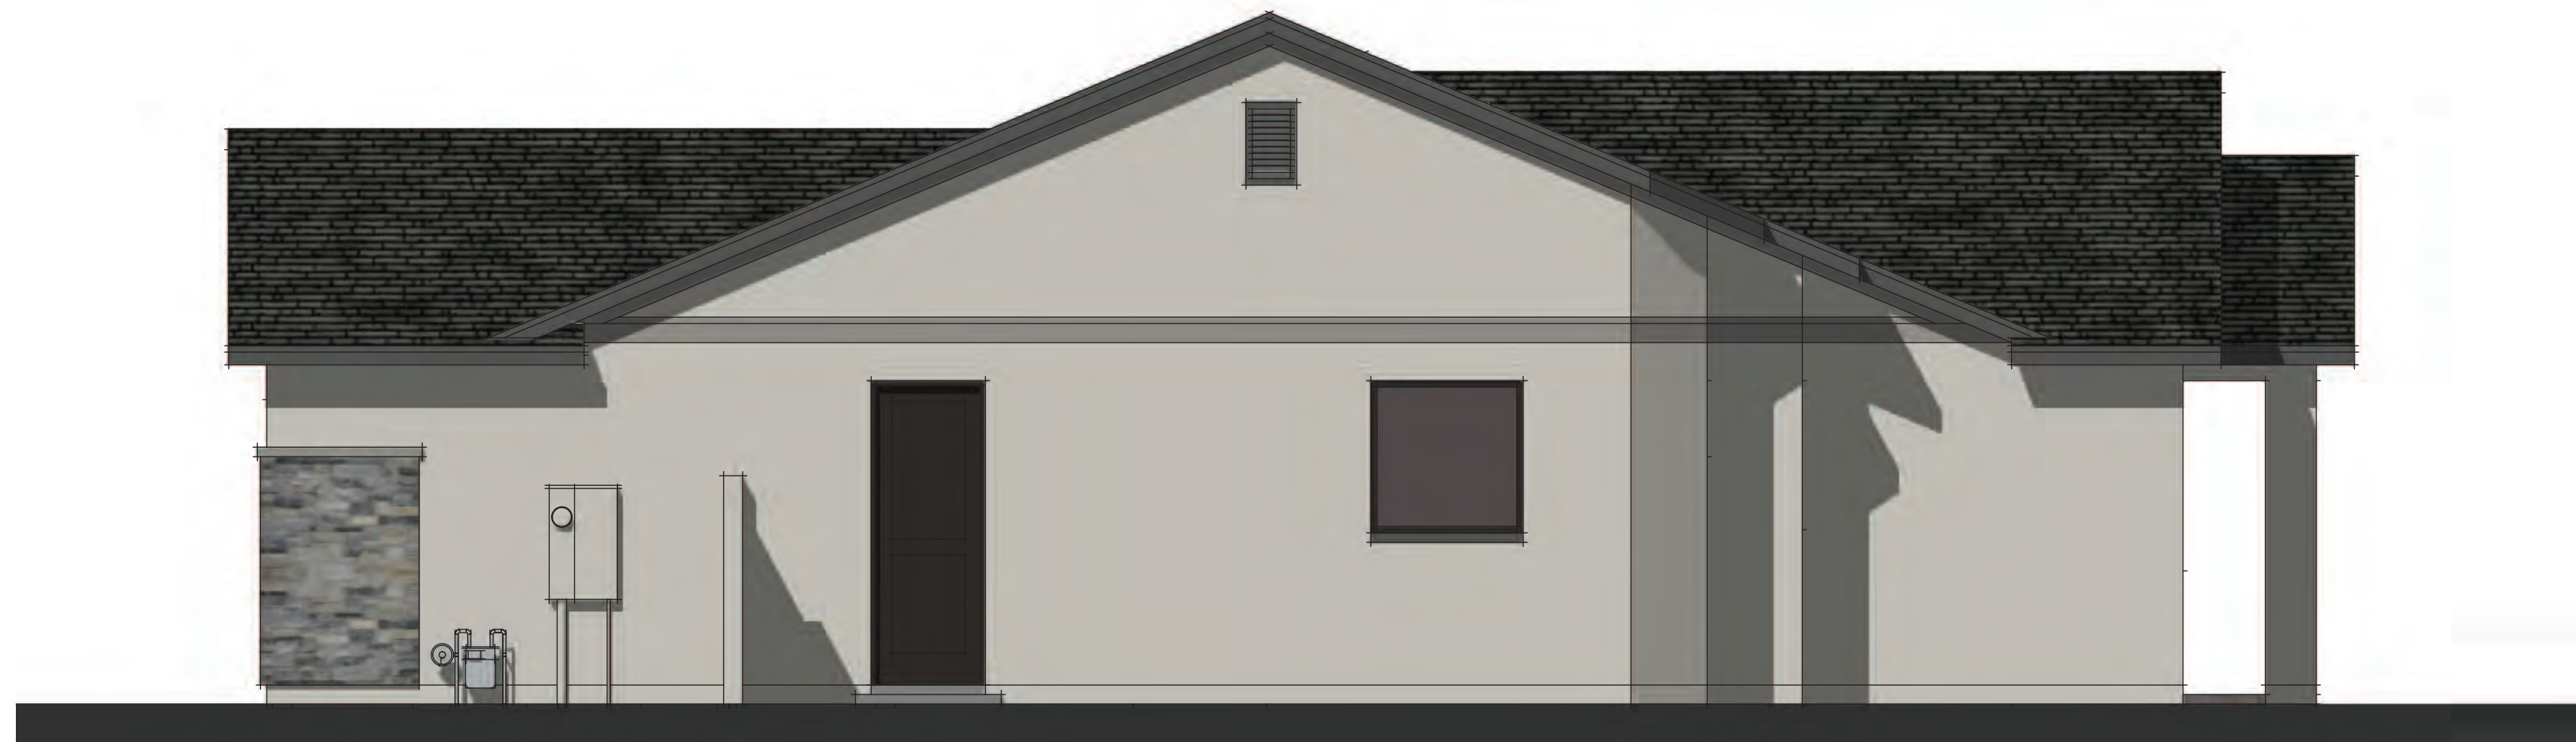

RIGHT ELEVATION
SCALE: 1/4" = 1'-0"



REAR ELEVATION
SCALE: 1/4" = 1'-0"



LEFT ELEVATION
SCALE: 1/4" = 1'-0"




FRONT ELEVATION
SCALE: 1/4" = 1'-0"






FRONT

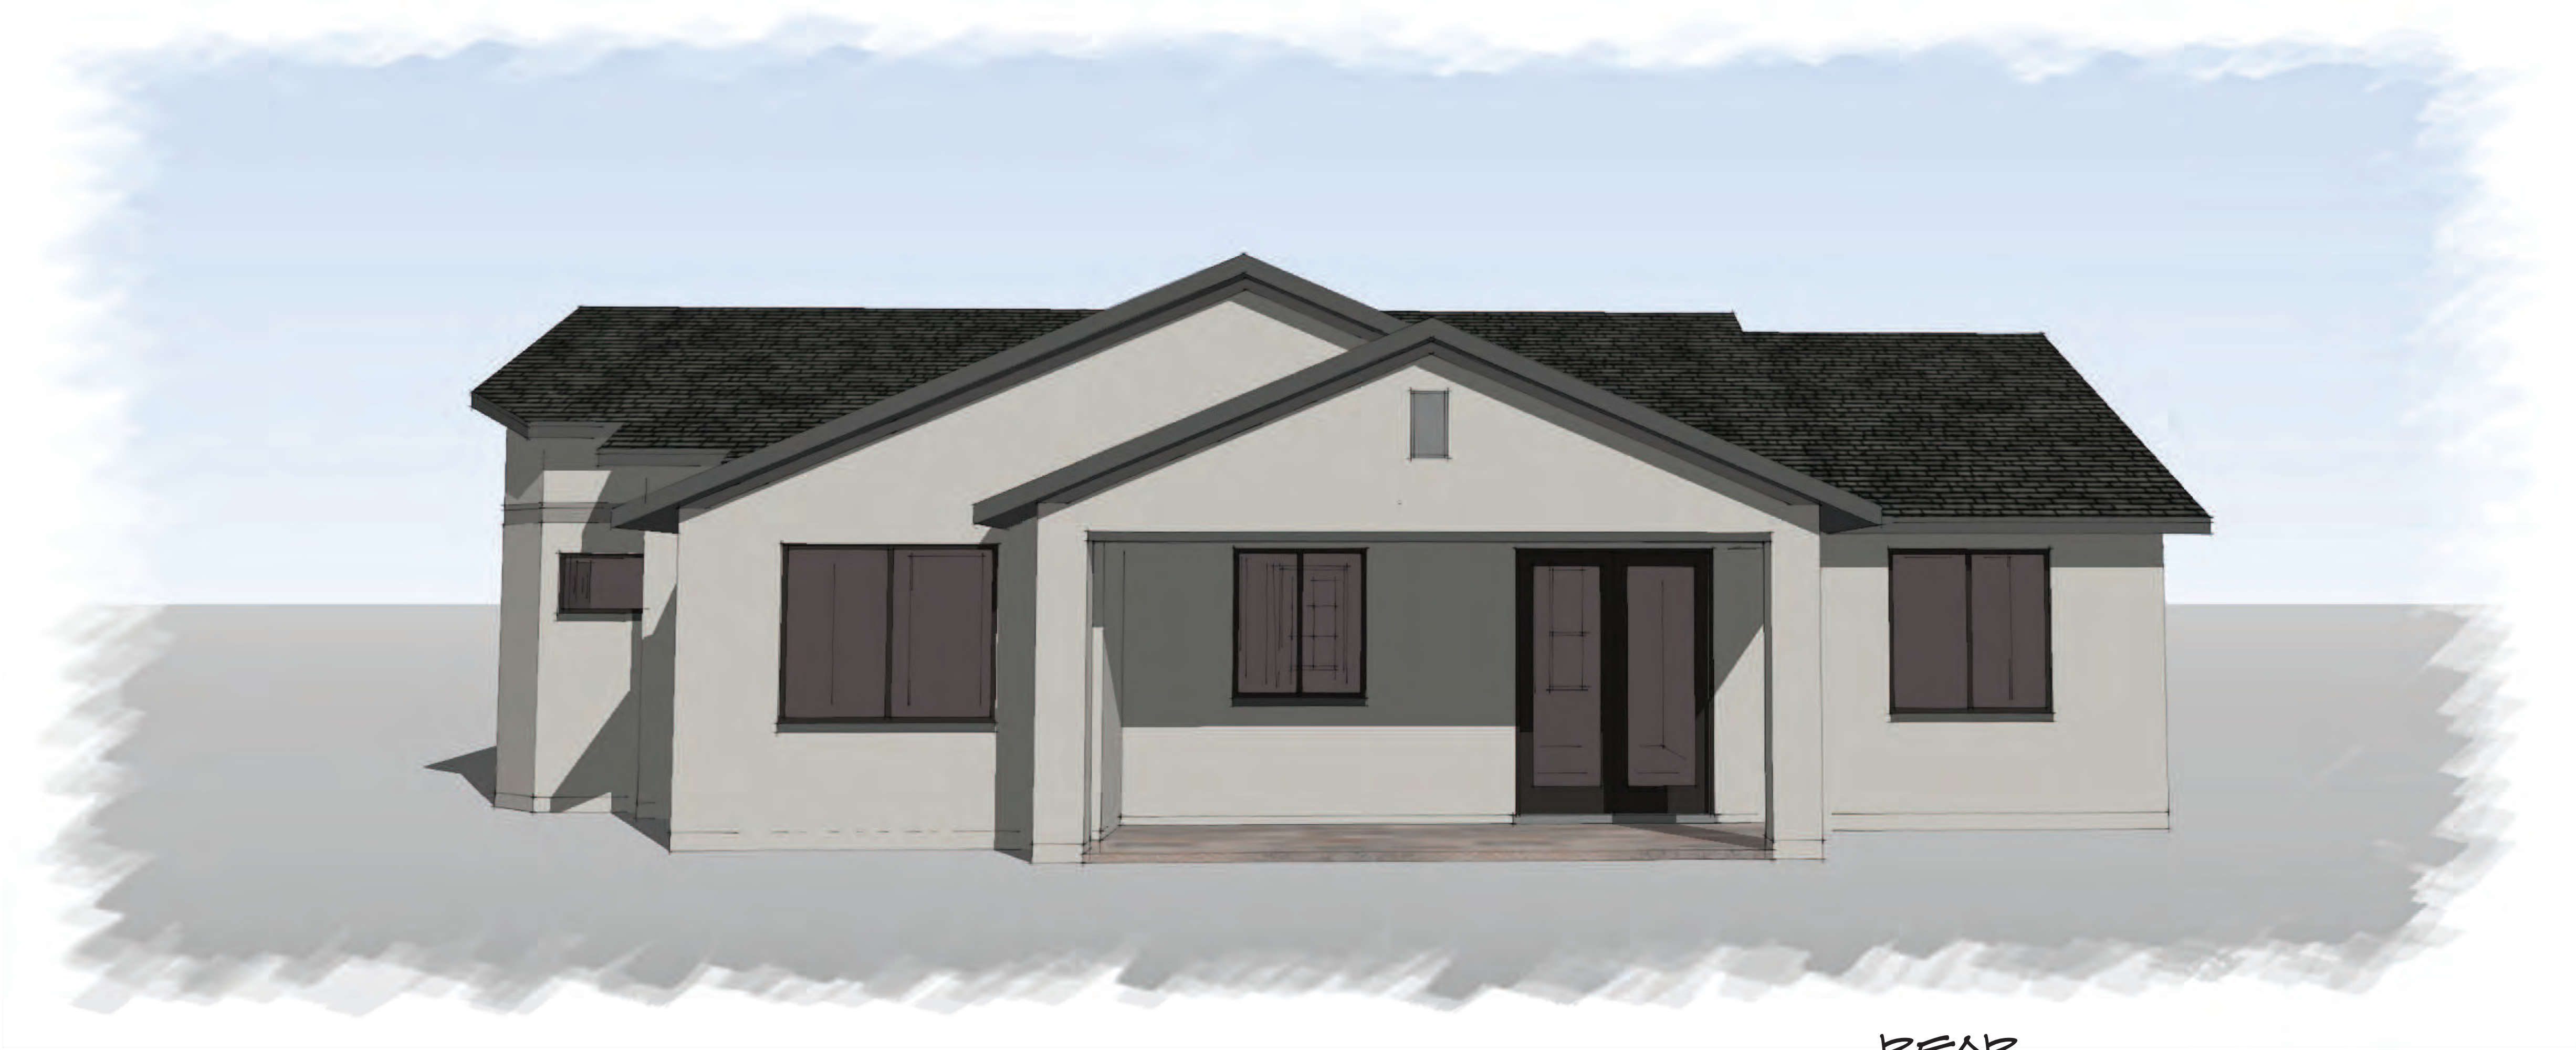

REAR

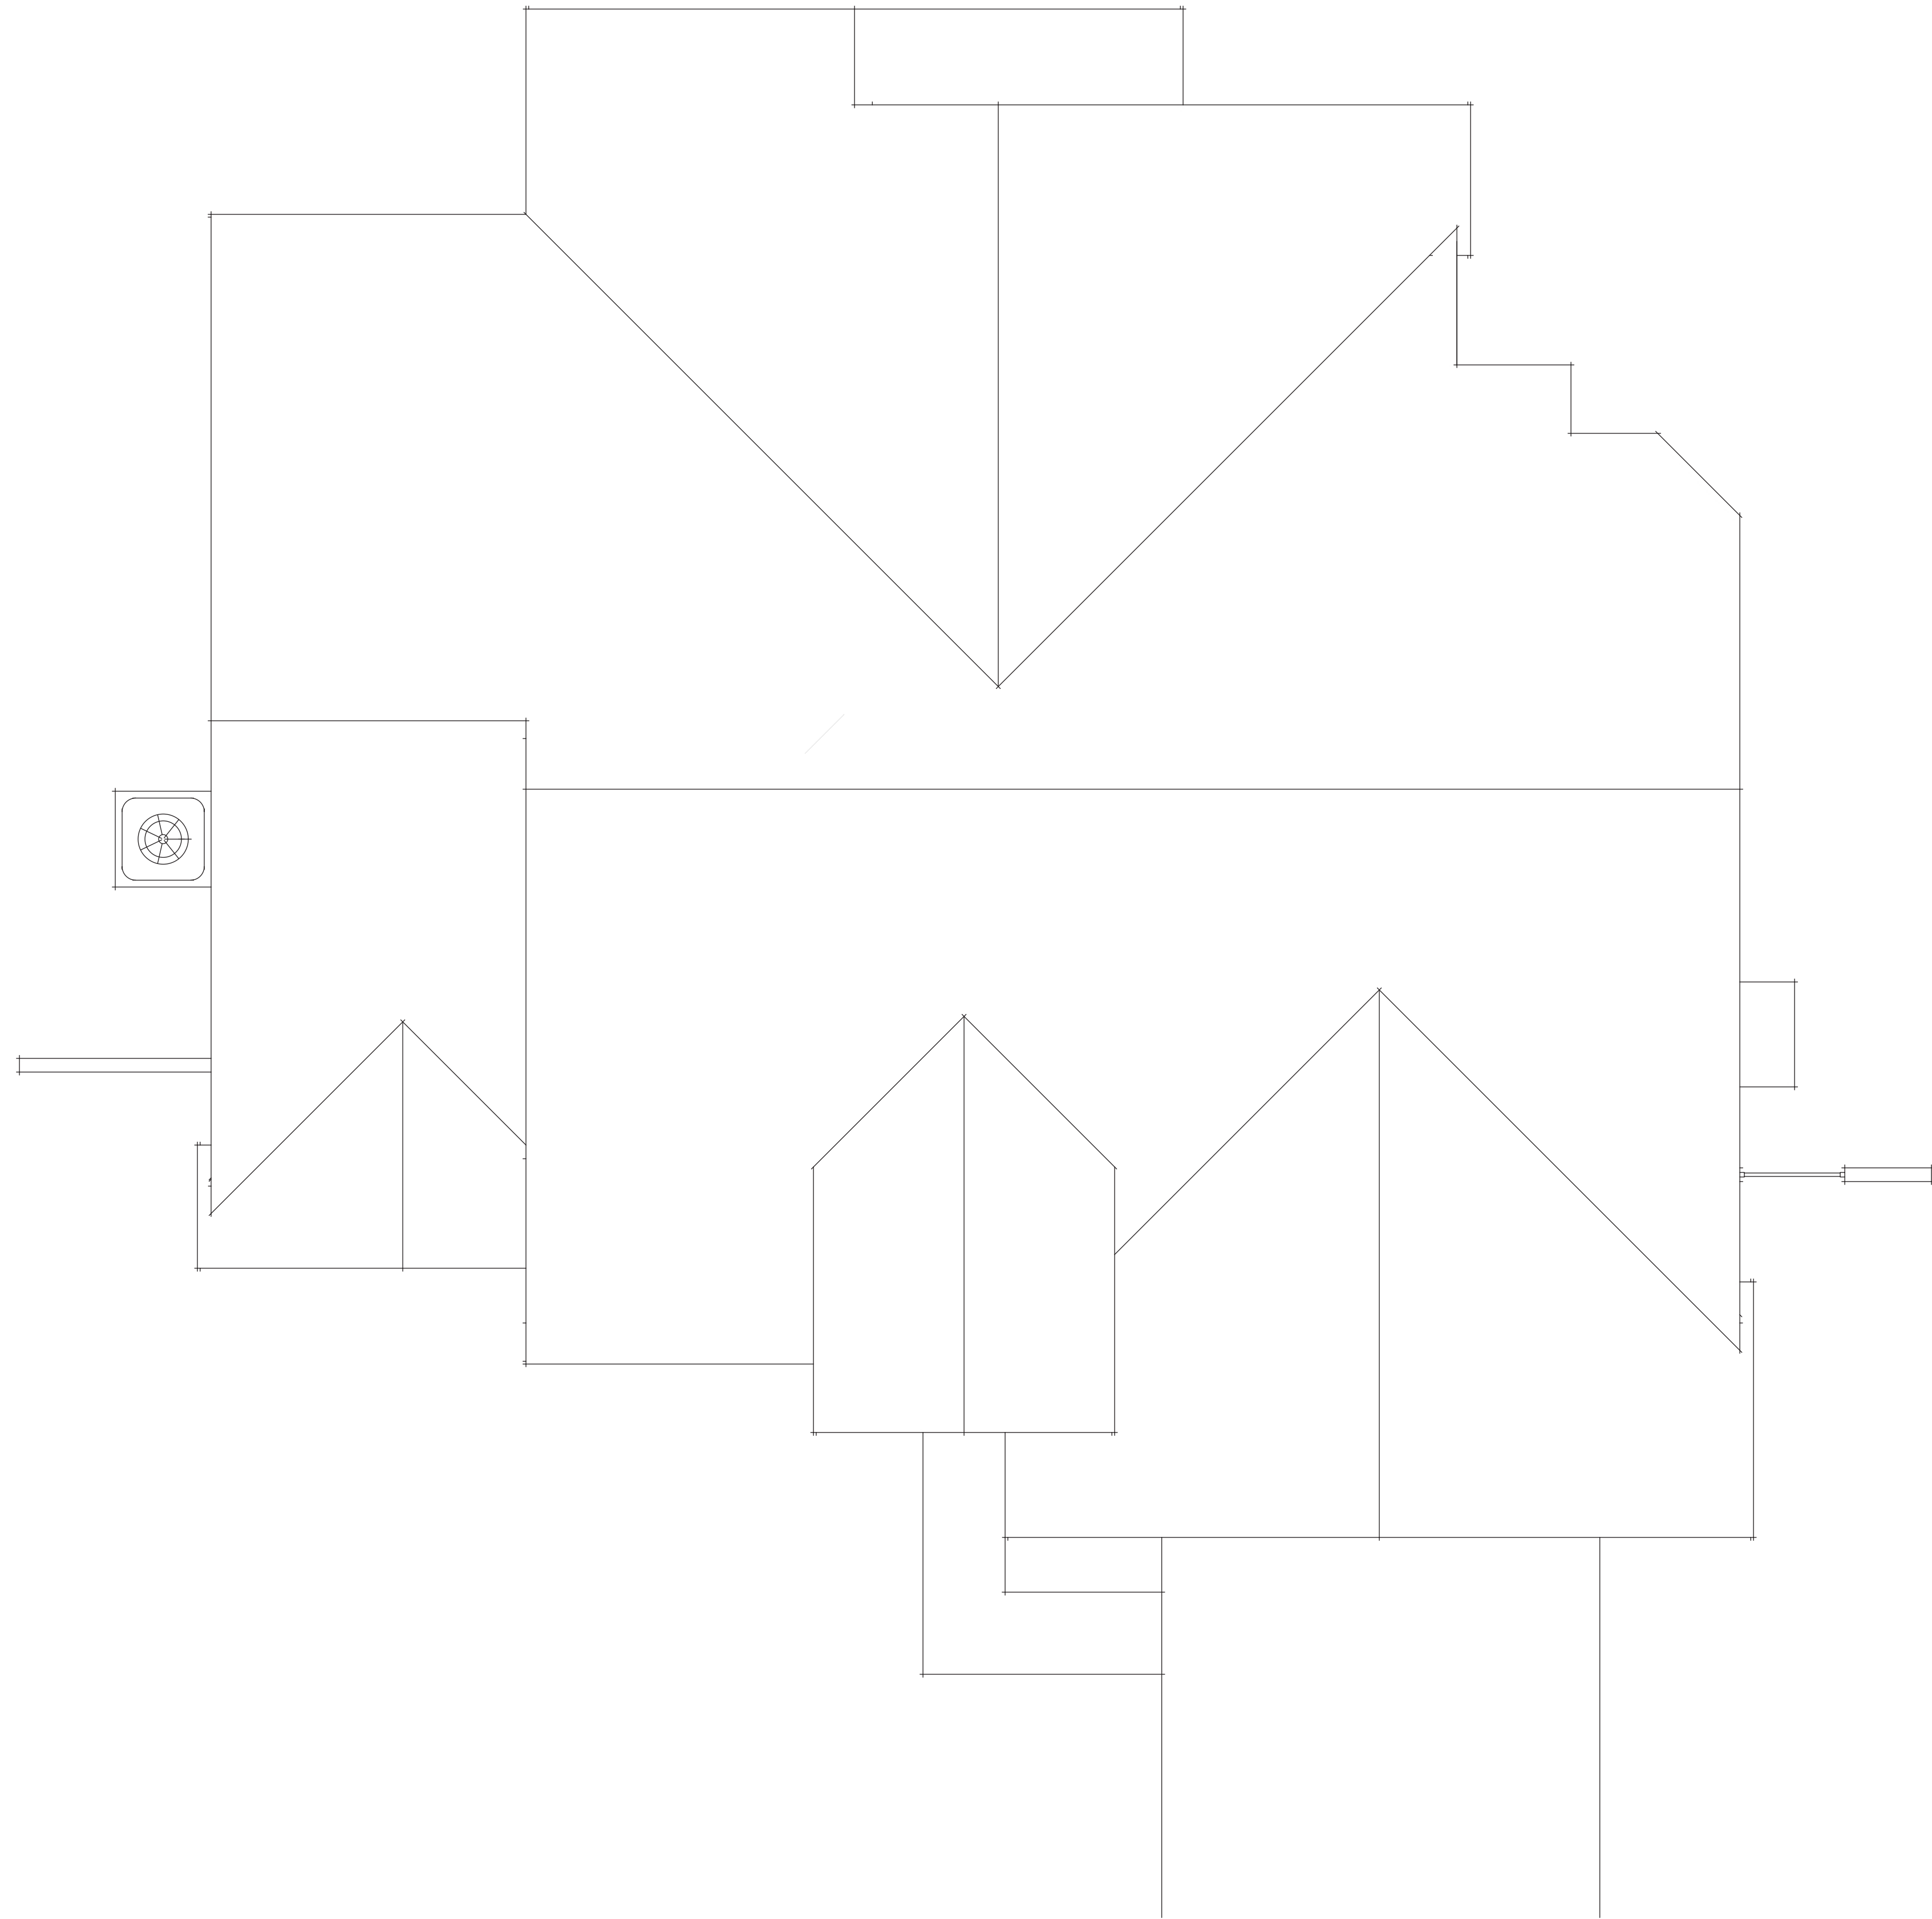

ROOF PLAN
SCALE: 1/4"=1'-0"